




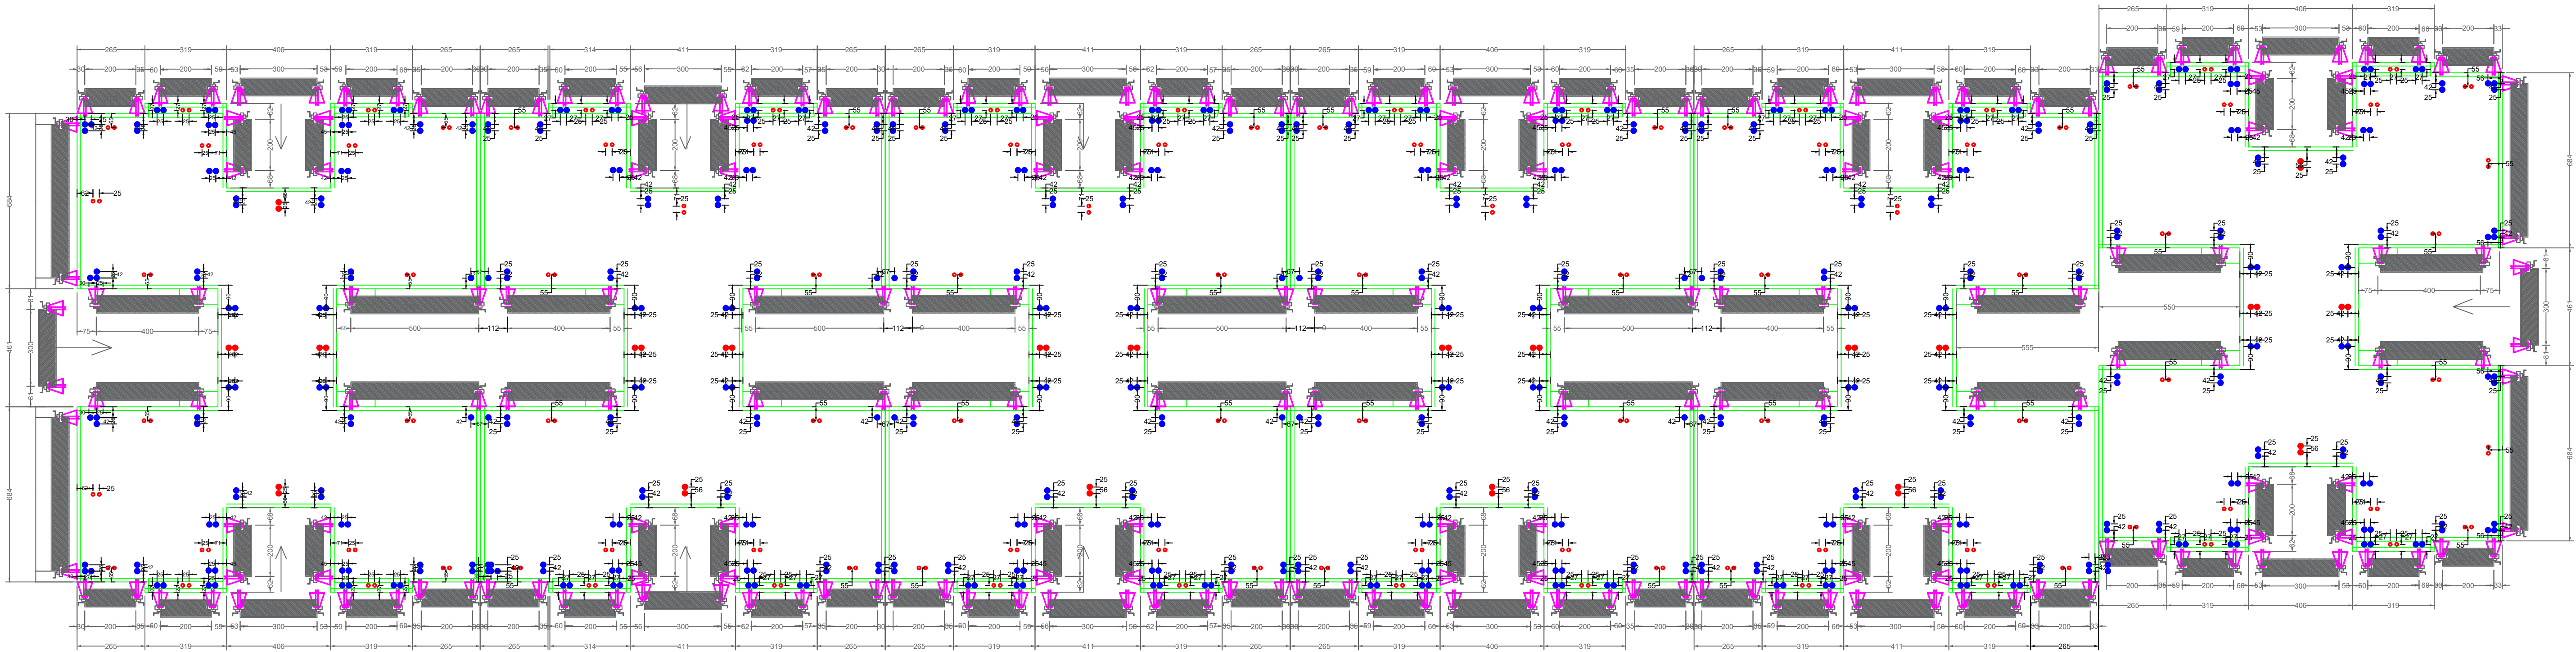


DET. DISTRIBUIÇÃO DOS PONTOS

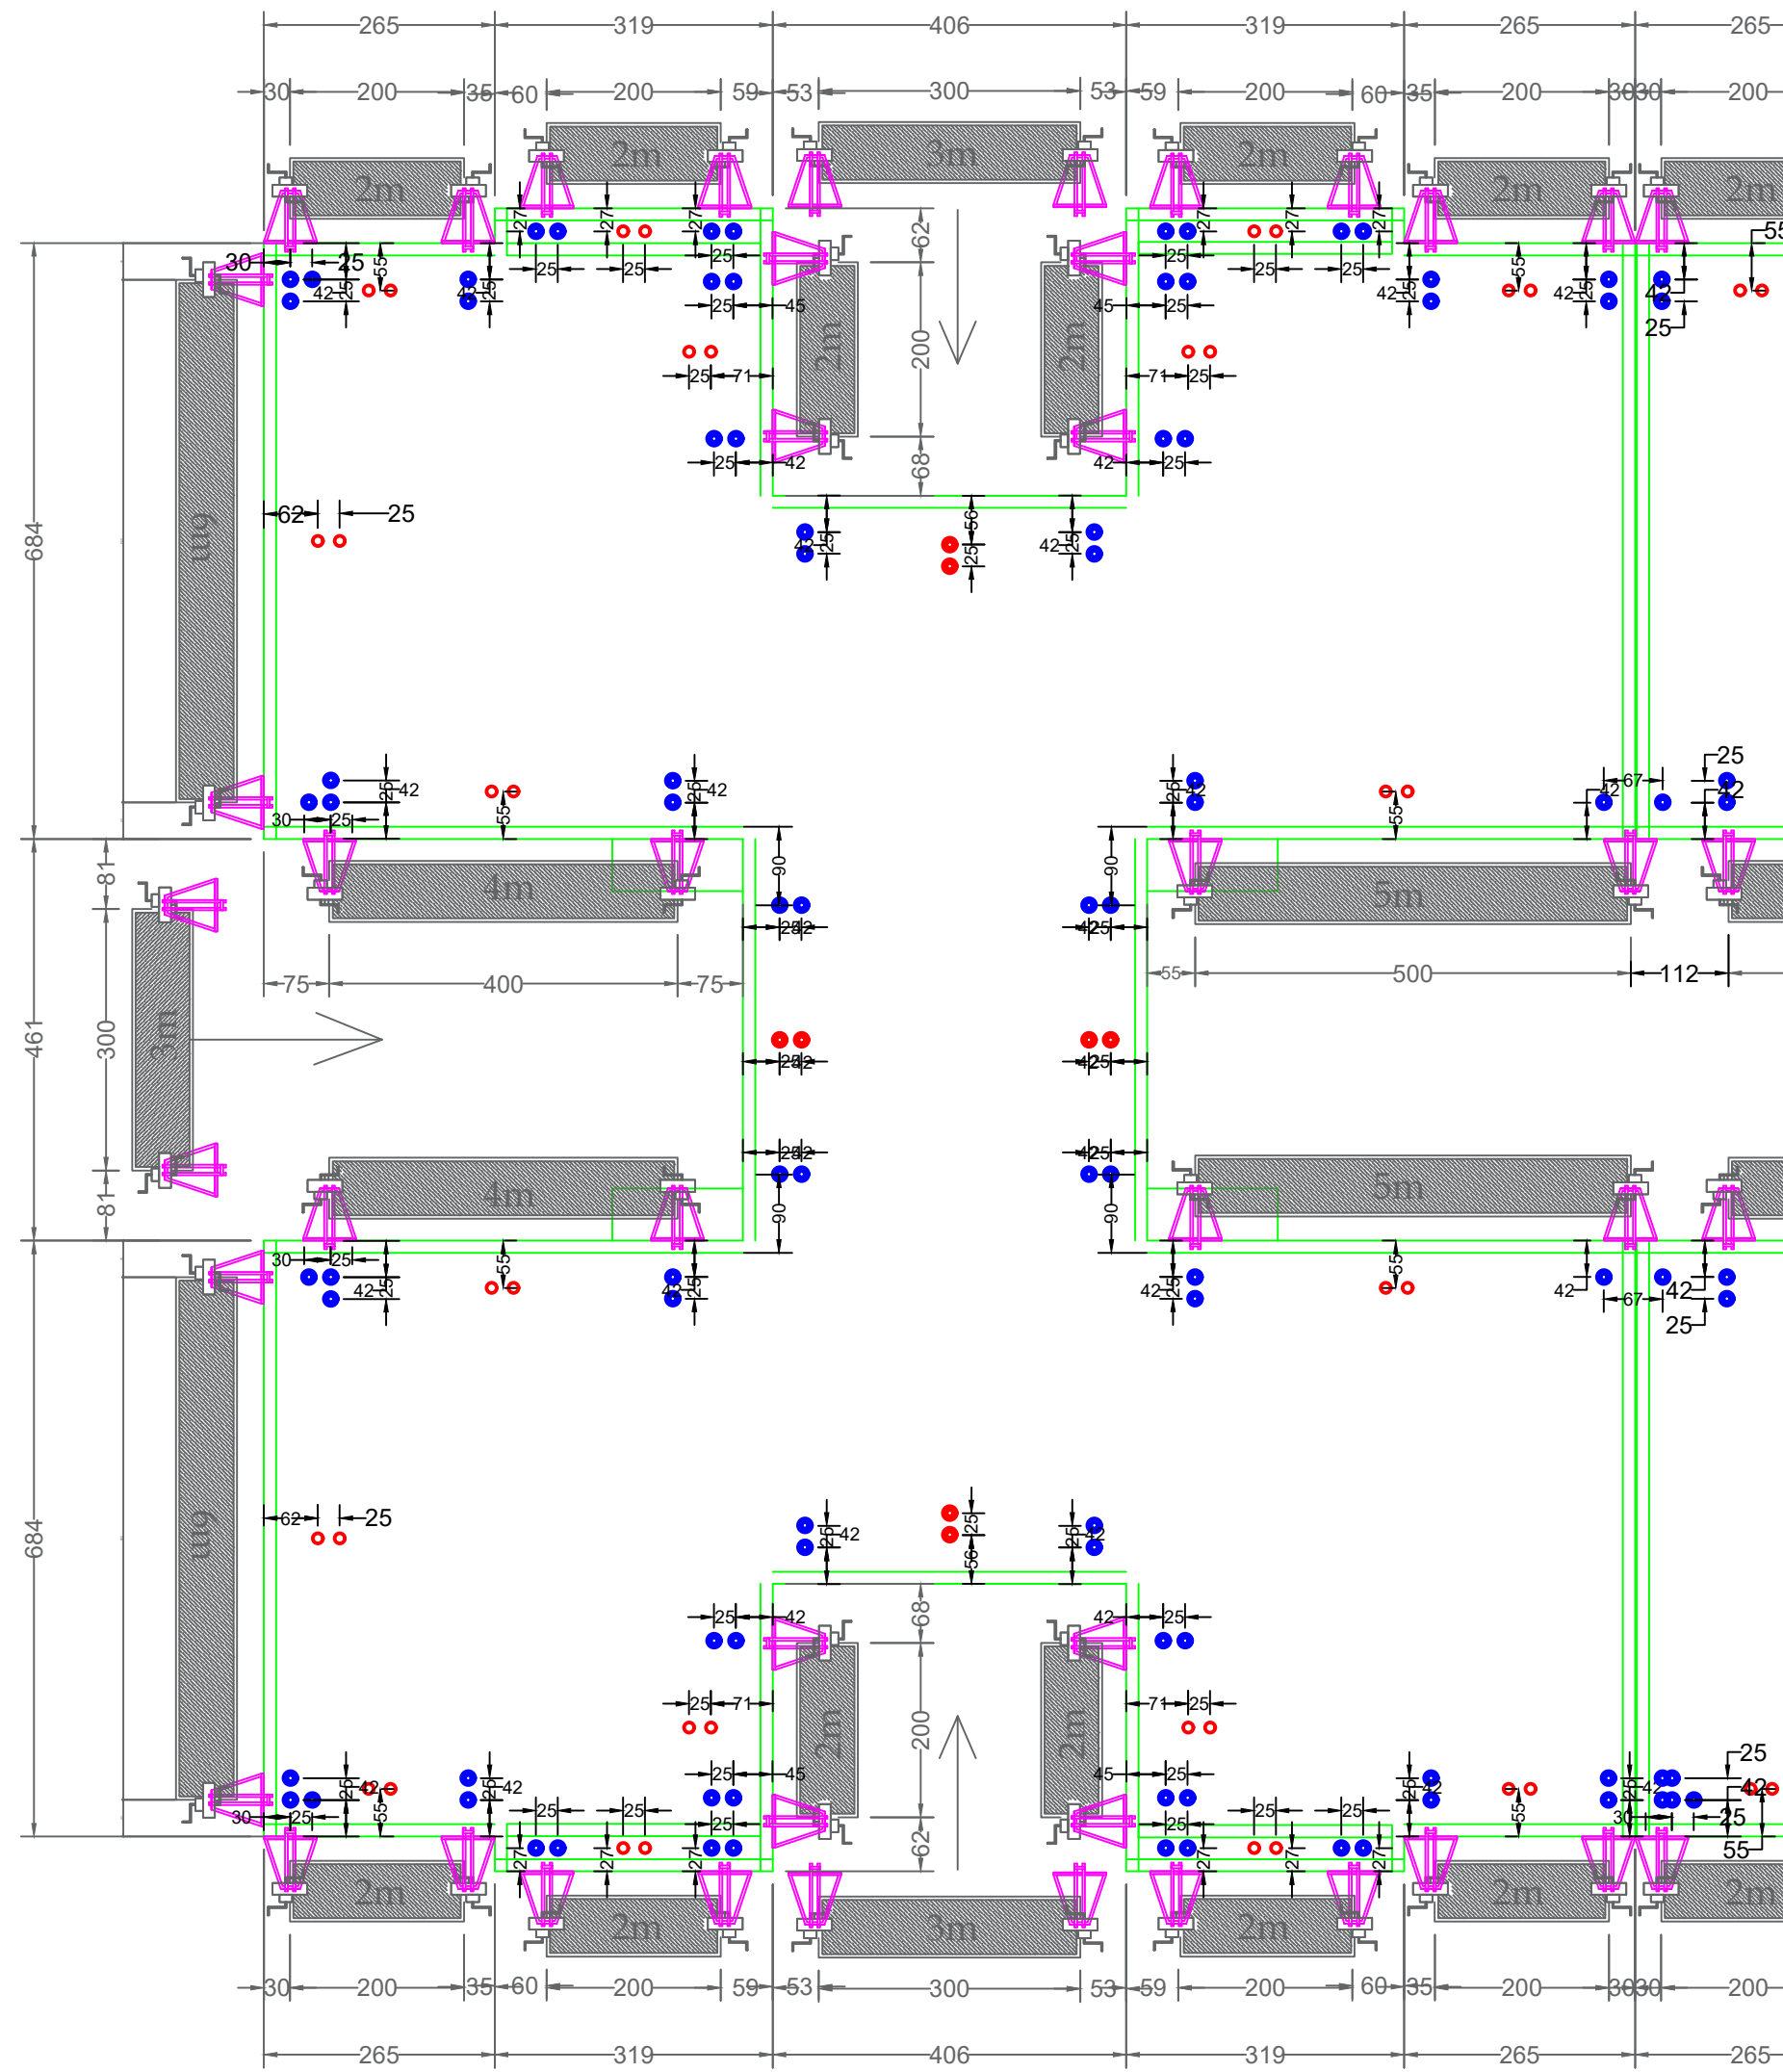

Torre 02 - MCM (x3) e MDP(x3)

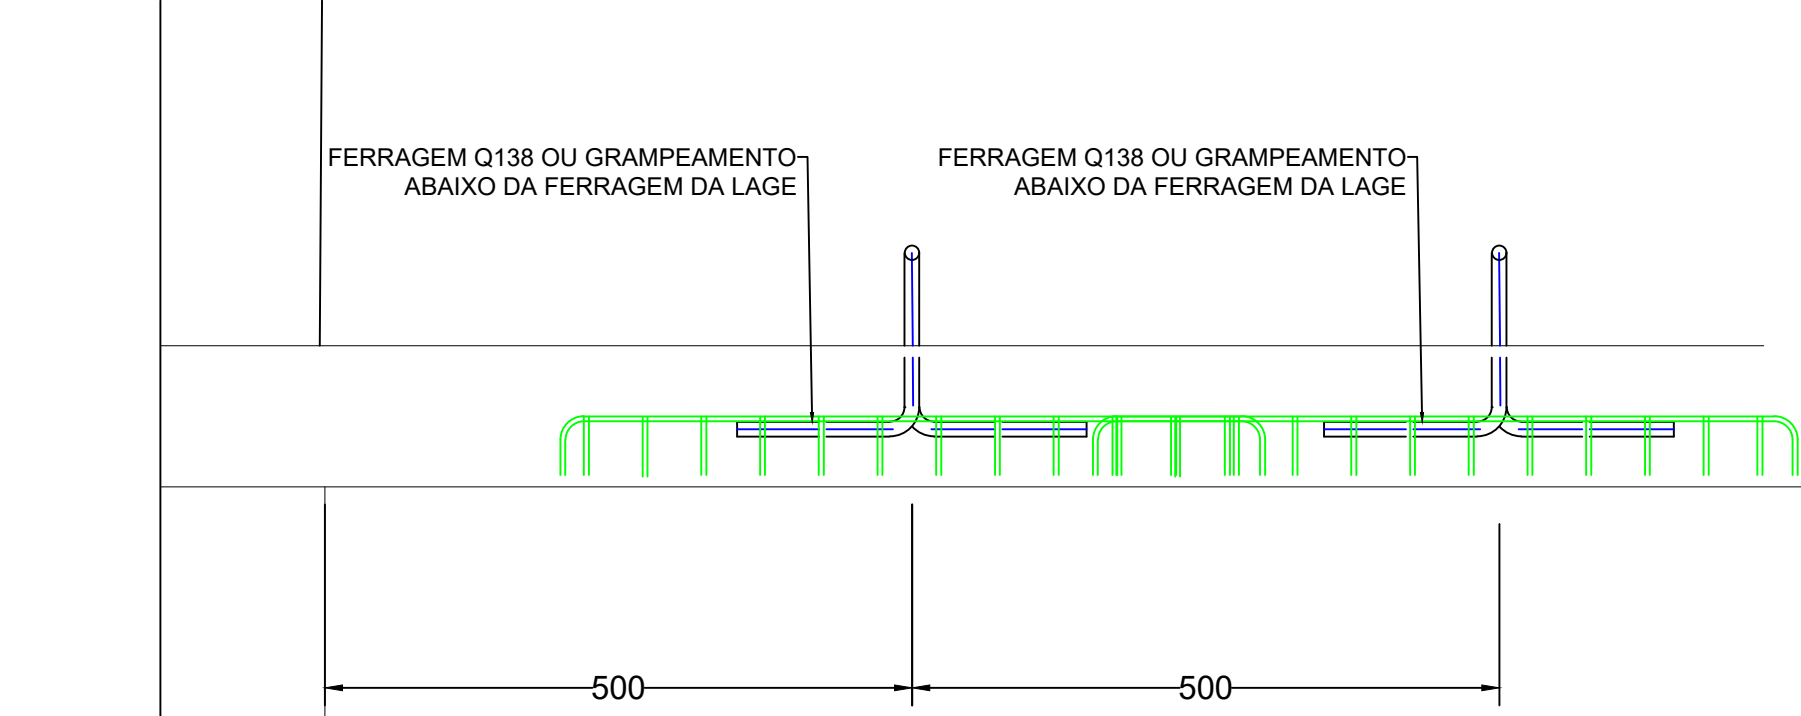

CLIPAGEM CORRETA

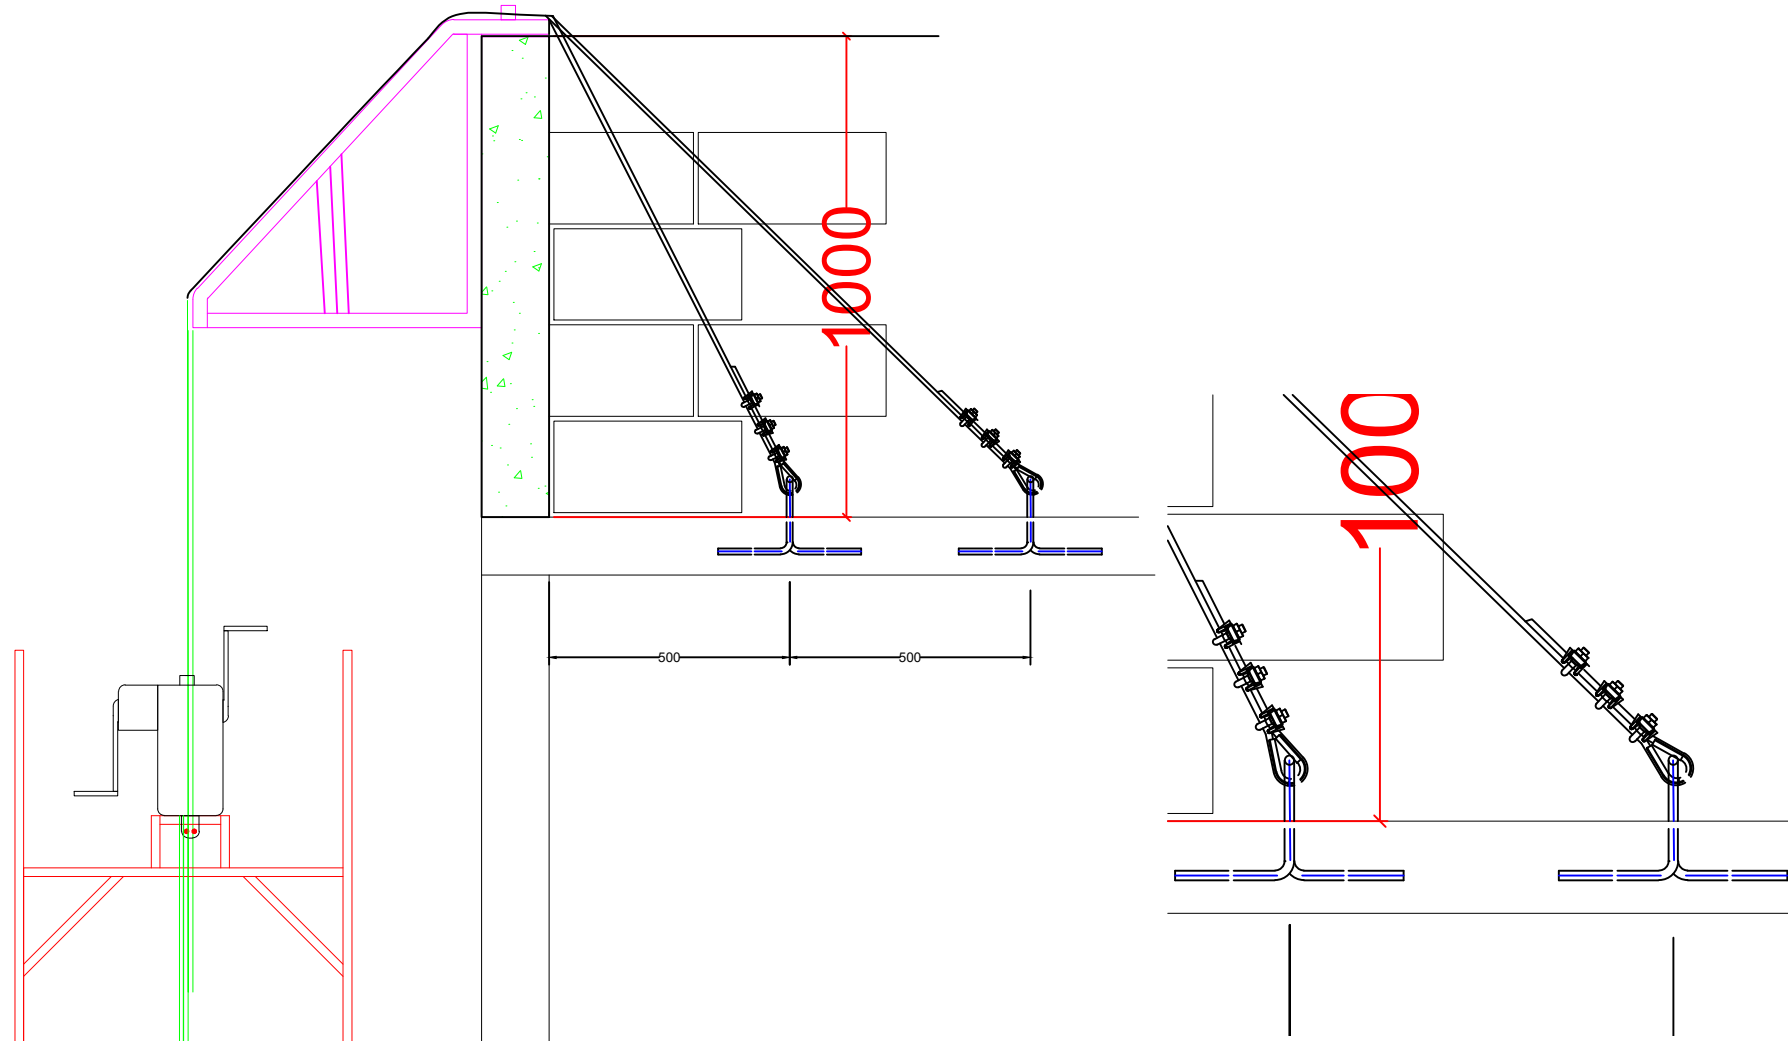

NOTA GERAL:
DECLARAMOS, PARA TODOS OS FINS, QUE O PROJETO APRESENTADO ATENDE AOS REQUISITOS NORMATIVOS DA ABNT NBR 15575, BEM COMO TODO O CONJUNTO DE NORMAS TÉCNICAS PERTINENTES À DISCIPLINA DE PROJETO EM QUESTÃO, E PROIBIDA A DIVULGAÇÃO DE QUALQUER MATERIAL SEM AUTORIZAÇÃO PRÉVIA. RESPEITE AS NORMAS VIGENTES

NºREV	DATA	DESCRIÇÃO	Responsável
01	14.04.2025	EMIÇÃO INICIAL	JOÃO OT.

REFERÊNCIA	ARQUIVO
14.04.2025	PFBVM18-RP350-EST-EX-T02-PL-LOC-R01 (1)

INCORPORAÇÃO E COTAÇÃO:	PROJETISTA
EMPRESAMENTO E LOCAL	SOLUÇÕES EM SEGURANÇA DO TRABALHO
PARC DAS ORQUÍDEAS	e-mail: joao@servicosdeengenharia.com
RIBEIRÃO PRETO - SP	celular / whatsapp: (16) 9 9242 - 8256

TÍTULO	001	001
TORRE PADRÃO	001	001
PONTO DE ANCORAGEM - INSTALAÇÃO	001	001
DISCIPLINA	DESENHISTA	RESPONSÁVEL TÉCNICO
MECÂNICA E	JOÃO OTÁVIO	ENG. MEC. JOÃO OTÁVIO
SEG. DO TRAB.		
REGISTRO COMPLETO DO ARQUIVO:	CONTRATO	DATA
PONTO DE ANCORAGEM		14.04.2025
		INDIC.

LISTA DE MATERIAIS POR BLOCO			
Nº	DESCRIÇÃO	APLICAÇÃO	QNTD
1	ANDAIME SUSPENSO	JOGO COMPLETO DE ANDAIME SUSPENSO	114
2	AFASTADORES	AFASTADOR PARA ANDAIME SUSPENSO	228
3	VERGALHÃO CA-50 Ø 1/2" EQUIP.	PONTO DE ANCORAGEM DE FIXAÇÃO DO AND. SUSP	456
4	VERGALHÃO CA-50 Ø 1/2" LINHA DE VIDA	PONTO DE ANCORAGEM PARA LINHA DE VIDA	228
5	PONTO DE ANCORAGEM AÇO INOX 316 1/2" -> P/4.000KGF	PONTO DE ANCORAGEM DE FIXAÇÃO DO AND. SUSP	456
6	PONTO DE ANCORAGEM AÇO INOX 316 1/2" -> P/4.000KGF	PONTO DE ANCORAGEM PARA LINHA DE VIDA	228